BERLIN-WESTEND · 1973–1979 · RALF SCHÜLER & URSULINA SCHÜLER-WITTE

ICC Berlin

INTERNATIONALES CONGRESS CENTRUM BERLIN

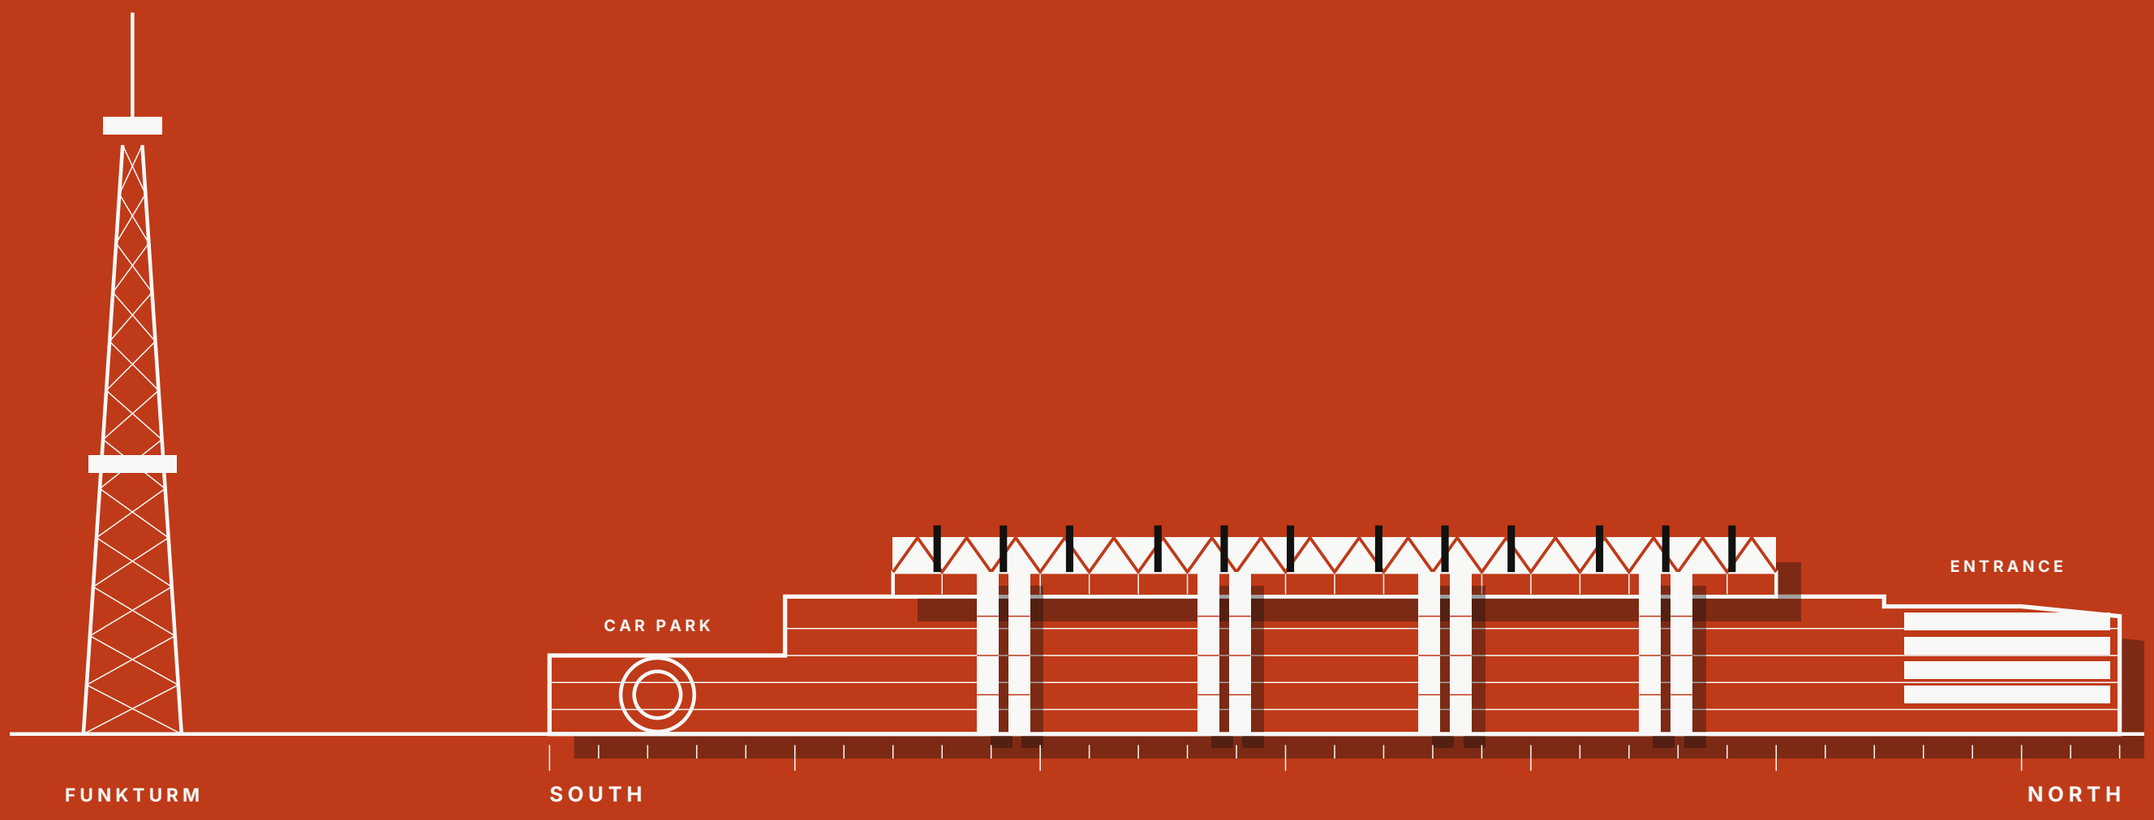

West elevation, schematic · about 320 m long, 40 m high · ticks every 10 m · Funkturm for scale

Twelve trusses on paired stair towers carry the casing over the two big halls. The inner building runs out at both ends.

IN NUMBERS

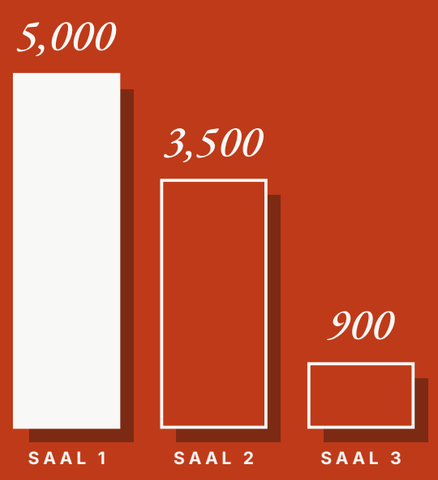

Seats, three largest halls

UP TO 20,000 PEOPLE

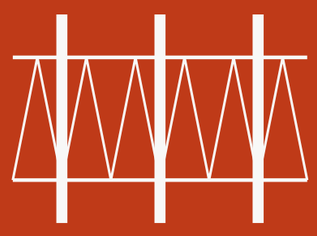

670 t

One group of three trusses

HEAVIER THAN THE FUNKTURM

13.79 m

26 piers carry the hall floor

13 PAIRS, 2.5 M ACROSS

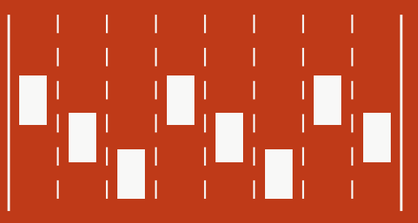

800

Cars per half hour, 8 lanes

AUTOFOYER DROP-OFF

TIMELINE

Sources: Landesdenkmalamt Berlin, Erläuterungen zum Denkmal ICC (2019), pp. 1–9; Denkmaldatenbank Berlin 09097889; BauNetzWoche 280 (2012); Senatsverwaltung press releases, 24 June and 2 September 2026; Wikipedia (Funkturm height). Drawings schematic.

SIANAARCHITECTURE.COM

Siana Architecture