BERLIN-WESTEND · 1956–1958 · LE CORBUSIER

Unité d'Habitation

TYP BERLIN · CORBUSIERHAUS · FLATOWALLEE 16

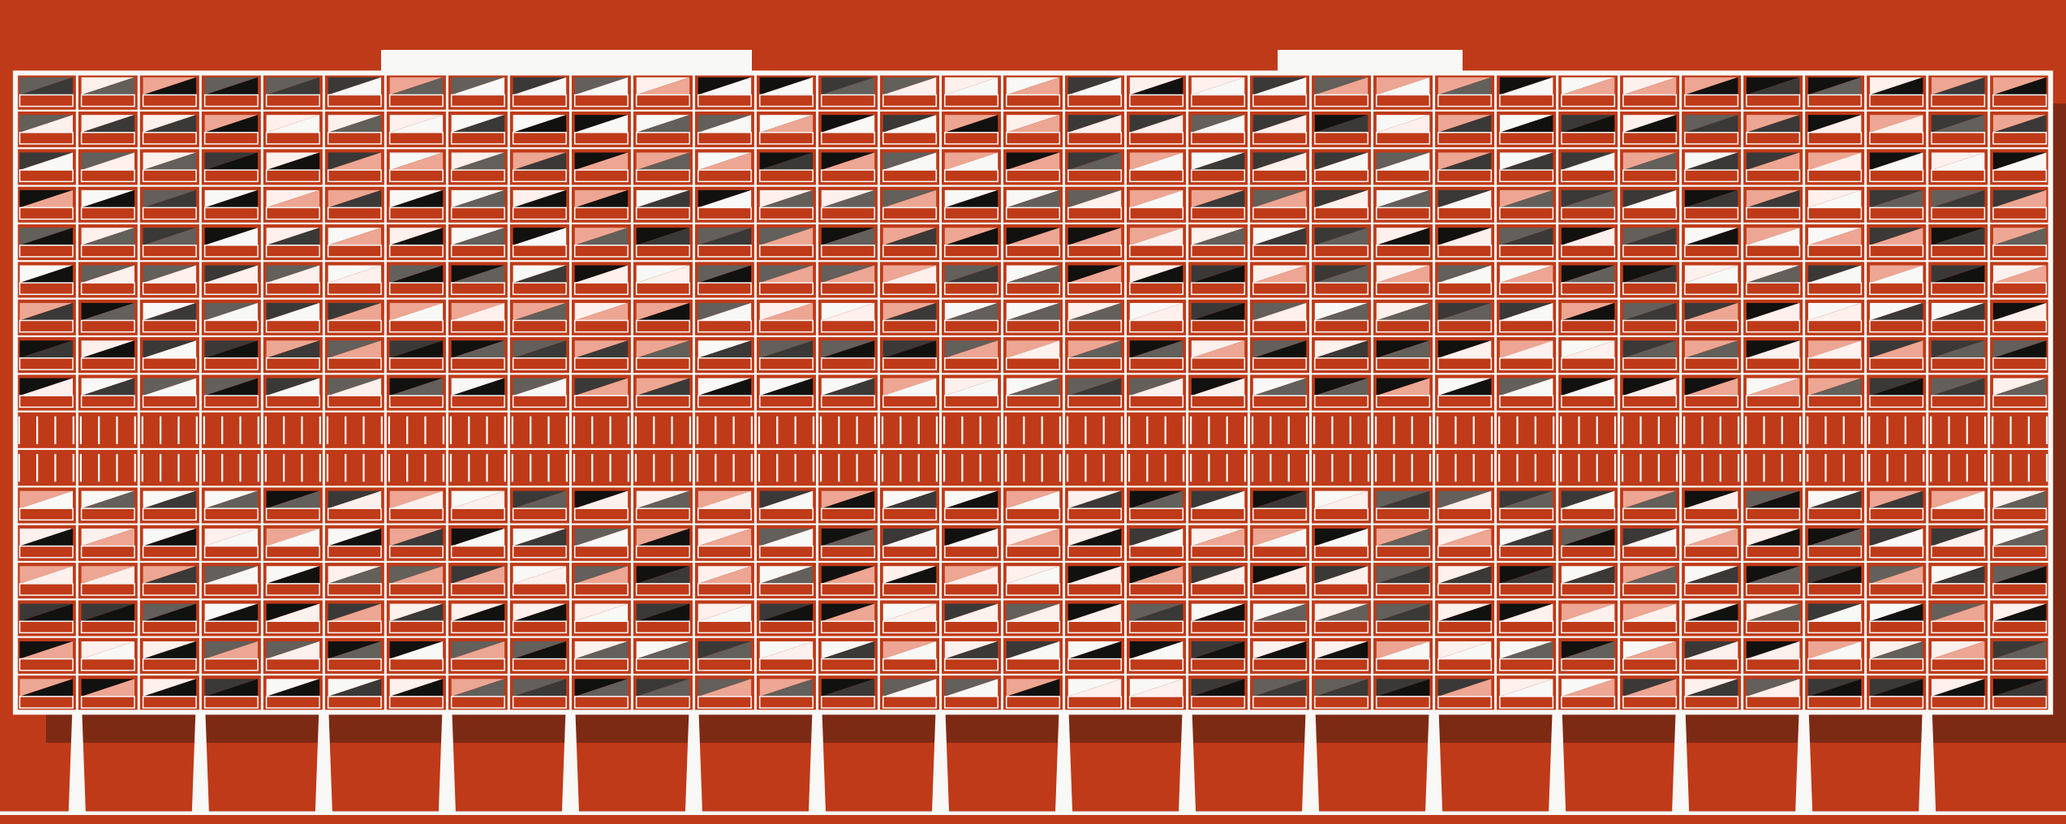

NORTH — SOUTH

West elevation · 141.2 m long · 52.9 m high · 17 storeys on a 7 m open ground floor

Loggias carry a colour each. Sunshade louvres replace them on the 7th and 8th floors.

SCHEMATIC: AXIS COUNT, LEGS AND ROOF PIECES SIMPLIFIED, COLOURS STAND IN FOR THE ORIGINAL HUES

IN NUMBERS

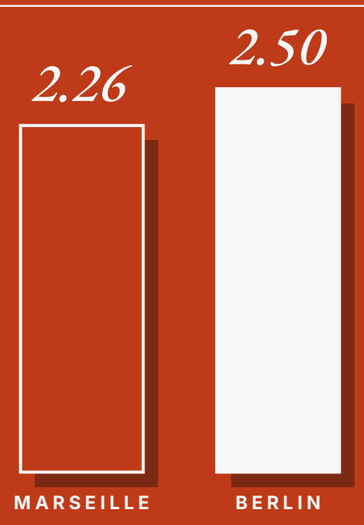

Metres floor to ceiling

THE CEILING FIGHT

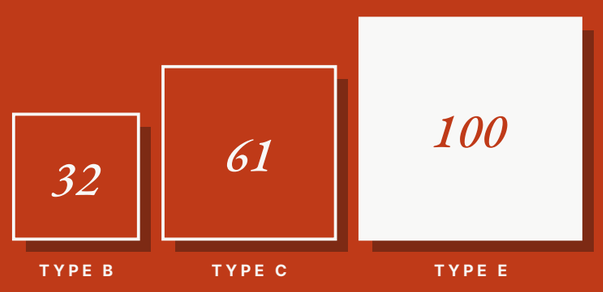

Square metres per flat type

FLAT SIZES

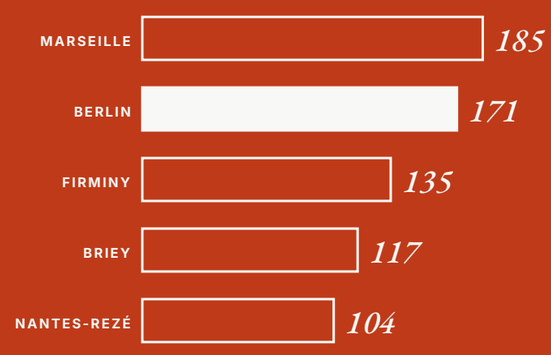

Thousand cubic metres, built volume

THE FIVE UNITÉS

Million DM, building, land, servicing

WHAT IT COST

TIMELINE

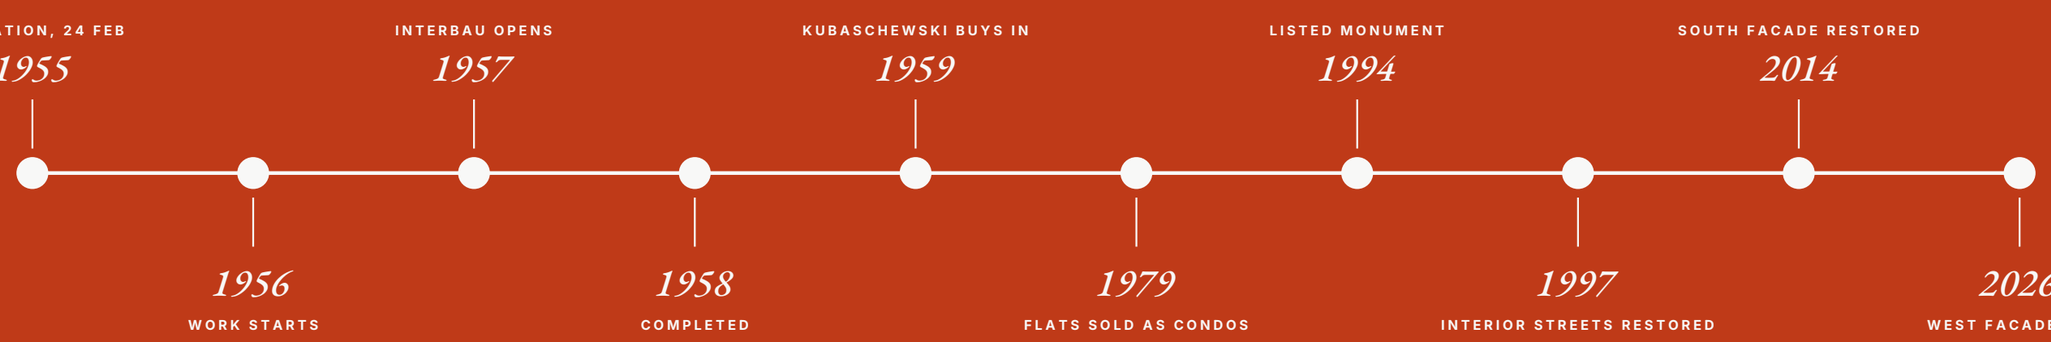

EVENTS EVENLY SPACED, NOT TO SCALE

Sources: Denkmalpflegeplan Corbusierhaus (Beer Architekten 2005), pp. 3–8, 13, 19, 35, 82; Denkmaldatenbank Berlin 09040533; Högner 2020, p. 106, Graf and Bauwelt via de.wikipedia „Corbusierhaus"; haustechnik-corbusierhaus.info. Drawing schematic.

SIANAARCHITECTURE.COM

Siana Architecture