BERLIN-STEGLITZ · 1971–1976 · RALF SCHÜLER & URSULINA SCHÜLER-WITTE

Bierpinsel

TURMRESTAURANT STEGLITZ

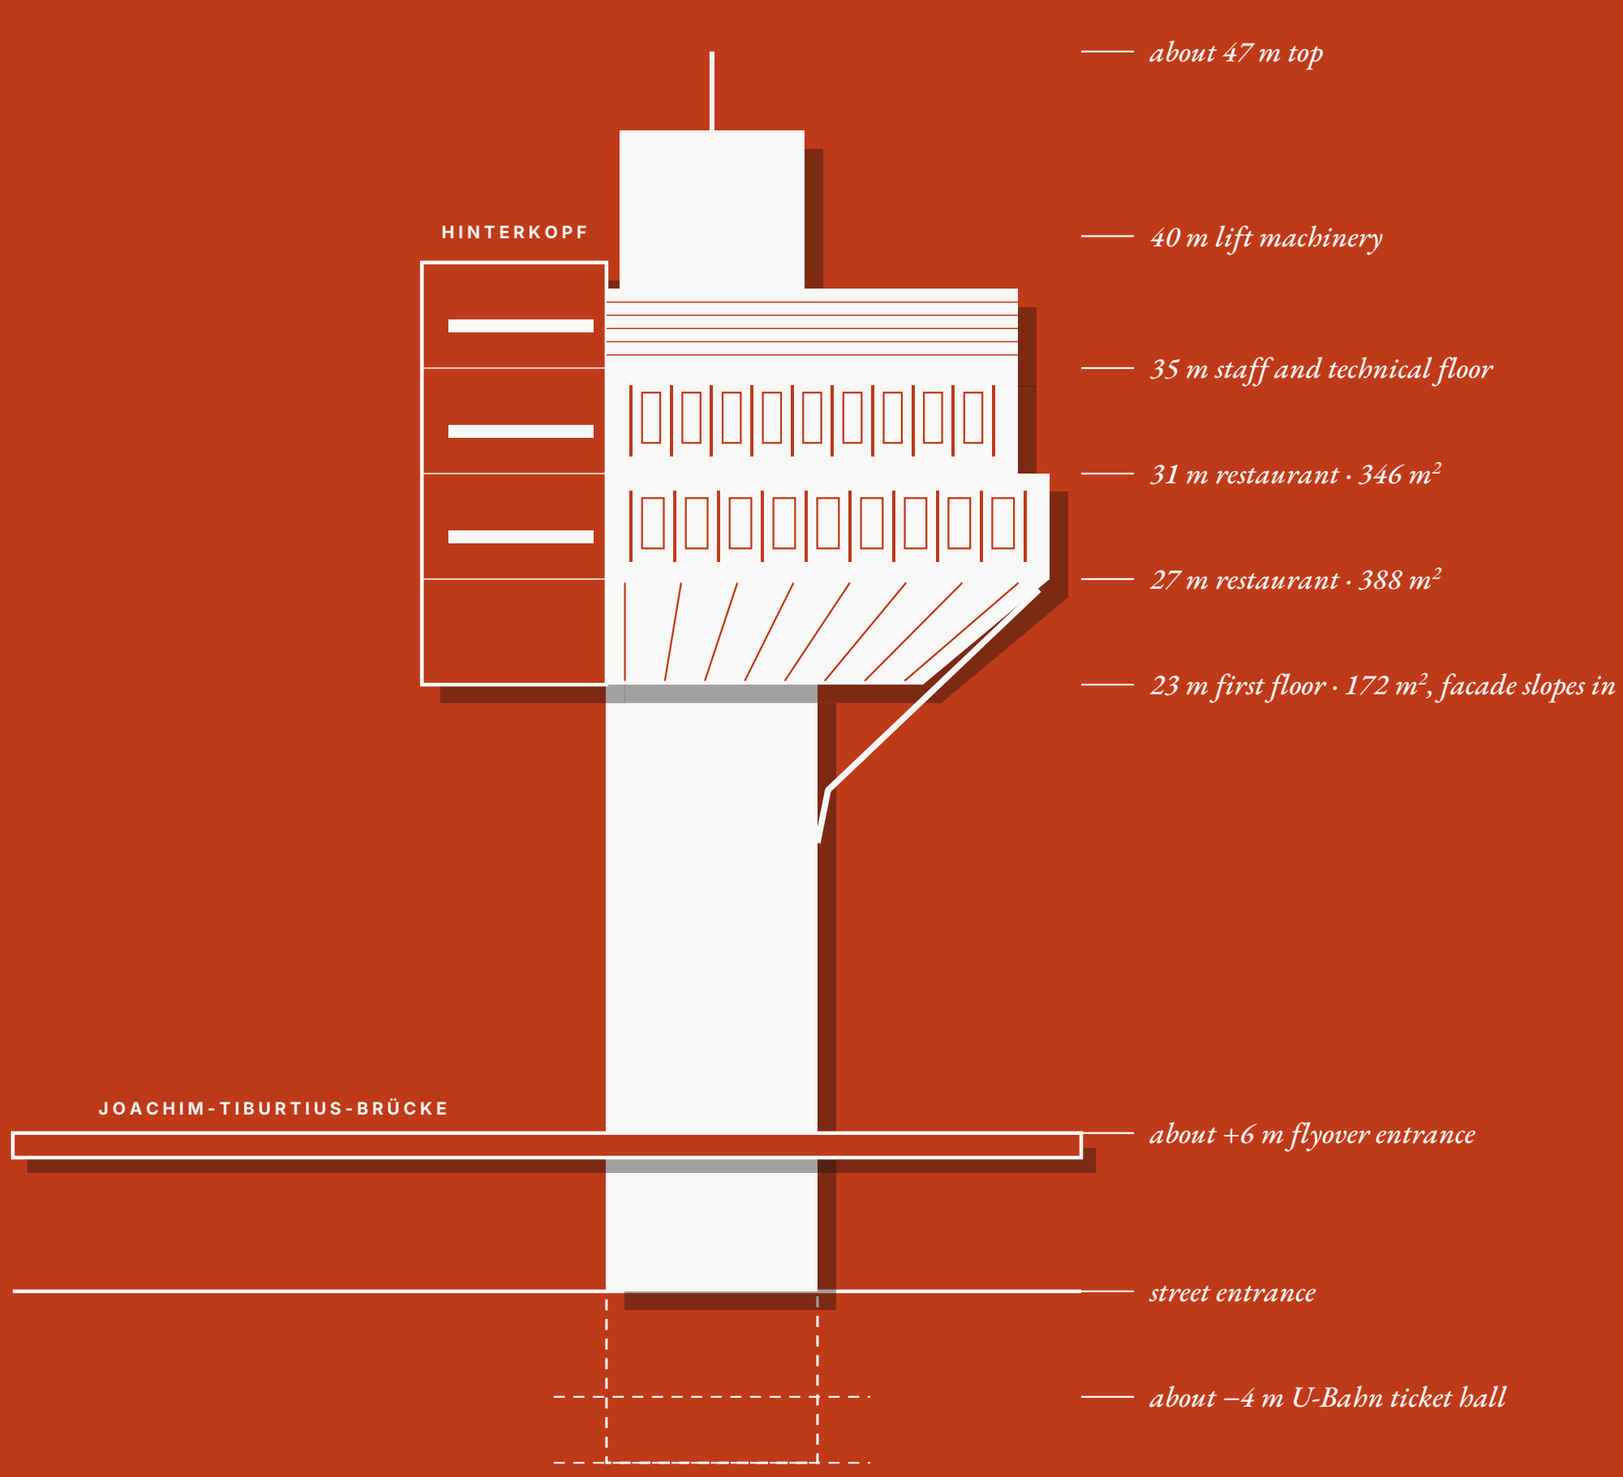

Side elevation, schematic · heights to source · widths estimated from the floor areas

Ten steel struts, bent at the shaft, carry the head. The service block on the left balances it.

IN NUMBERS

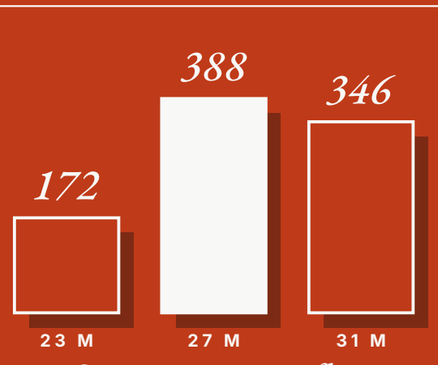

Square metres per floor

MIDDLE FLOOR LARGEST

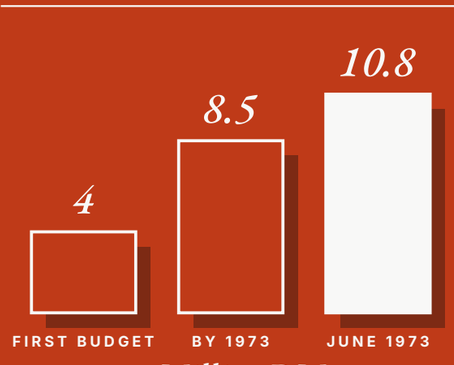

Million DM

COST GROWTH

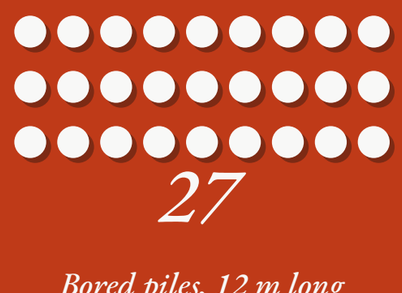

Bored piles, 12 m long

1.30 M ACROSS, UNDER A 3 M SLAB

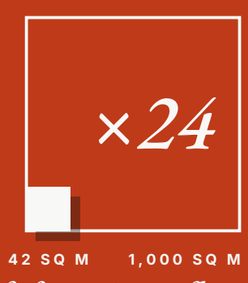

Shaft footprint to floor space

ABOUT 24 TIMES

TIMELINE

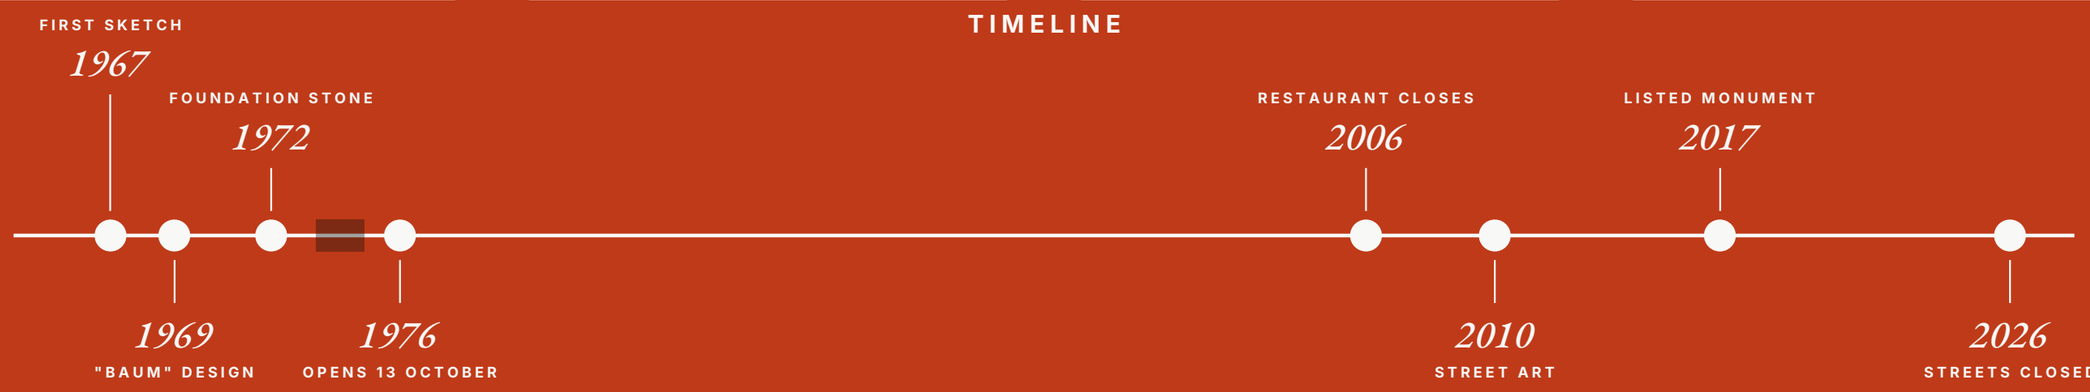

Sources: Foljanty, Der Verkehrsknoten Steglitz (TU Berlin 2011), pp. 25–78; Denkmaldatenbank Berlin 09097832; Berliner Morgenpost, 27 January 2017; Bezirksamt Steglitz-Zehlendorf, 21 October 2026; Wikipedia. Drawings schematic.

SIANAARCHITECTURE.COM

Siana Architecture